

2025

NATHANIA JIFIA



Interior Design

Portfolio



About Me

An interior designer with over four years of design experience and a strong background in architecture and digital marketing. Passionate about creating visuals that communicate stories and ideas, supported by strong creative problem-solving and communication skills that help expand my professional network. A fast learner dedicated to delivering high-quality results and continuously grow as a designer.

EDUCATION:

TARUMANAGARA UNIVERSITY / Architecture **2021**
Qualify for Scopus index International Journals in Interior
SMAK 1 PENABUR Jakarta **2017**

CONTACT:

nathaniajifia@gmail.com
+6281219763238

LANGUAGE:

English – B2, certified by IELTS, British Council
Mandarin – HSK 2 / elementary beginner level
Bahasa – Native

KEY SKILL:

Visual Storytelling

Design Layout

Sketchup

AutoCad

Enscape

Adobe Photoshop

Microsoft Office

IN-HOUSE INTERIOR DESIGNER

PT ARWANA CITRAMULIA, 2023 – PRESENT

- Developed design concepts and technical drawing for in-house projects using Sketchup and AutoCad
- Designed impactful presentation decks and visual proposals for the company executives and client presentation
- Translated design concepts into professional visual storytelling
- Reviewed building design and detail based on project plan and layout
- Supervised construction progress and conducted routine site visit
- Coordinated closely with the Head of Design and collaborated with vendors to ensure accurate implementation of design concepts
- Selected materials that met aesthetic and budgetary requirements
- Performed ad hoc tasks to support design and marketing projects, include participating at Arch:ID for the past two years as a merchandiser

CONTENT STRATEGIST

BOGA GROUP, 2022 – 2023

- Led content strategy and creative direction for multiple F&B brands
- Developed design briefs for digital marketing materials
- Supervised a social media team consisting of a designer, content creator, and social media officer
- Collaborated with the marketing manager to create seasonal campaign
- Produced social media content and copywriting for the company's culture and lifestyle branding.
- Increased social media visitors by 908% and engagement by 2800% within 3 months through organic content
- Created trending videos with over 1 million views on Reels and TikTok
- Pitched new ideas to address digital marketing challenges

FREELANCE DESIGNER

SINCE 2021

- Designed two modern websites using WordPress and Figma
- Worked remotely with Singapore clients, producing and editing video content for SGGowhere (2024) and several YouTube projects (2021)



Nathania
Jifia

Interior Designer



Table of Content

About me	01
Table of content	02
Project 1 : M Living room – A residential project	03
Project 2 : Pavilion dining space	05
Project 3 : Countryside villa bedroom	06
Project 4 : In-House corporate project at Arwana	08
Project 5 : Vintage Photobooth installation	13
Project 6 : Blossom affair	14
Project 7 : Matcha café	15

PROJECT 01

M Living Room


Year 2024
Project Residential
Area 42 SQM

A modern, sophisticated living space that blends warmth and elegance. The high ceiling opens up the room, creating gentle lighting and a cozy atmosphere. Soft wood tones and dark marble come together to form a calm and contemporary atmosphere, perfect for relaxing or gathering with loved ones.







- ① **HPL - TACO**
TH 61 WM
Ash Zebrano wood matte
- ② **HPL - AICA**
WAKW-14714-KS83
Lioz Montemor
- ③ **HPL - TACO**
TH 014 AA
Light Grey

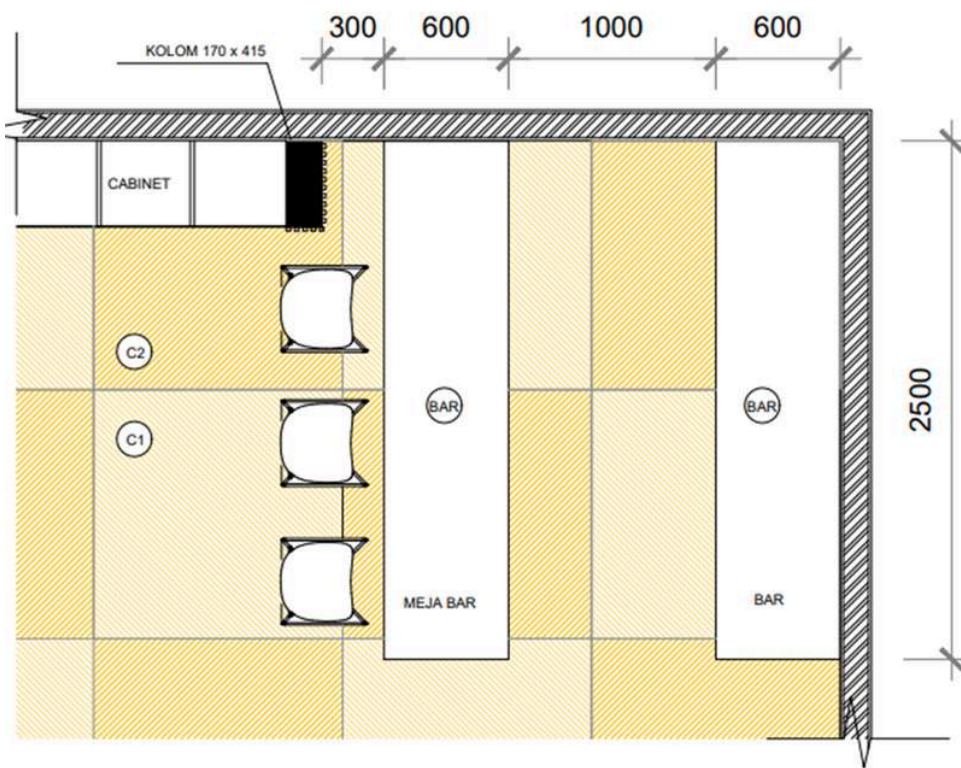

BAR AREA PLAN
SCALE 1 : 25

BAR TOP
(BAR) 600 X 2500 MM
(MARBLE TOP)

FLOOR CUT SIZES
C1 1200 X 1200 MM
C2 1200 X 1200 MM

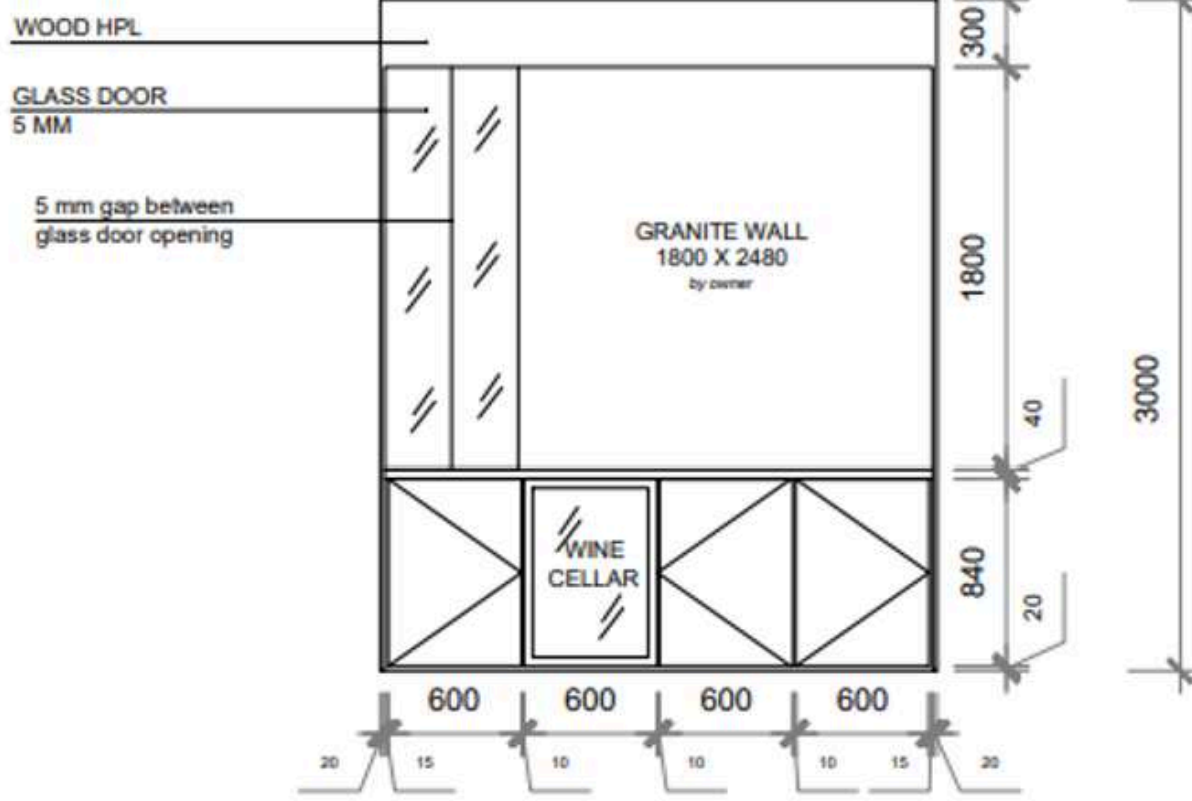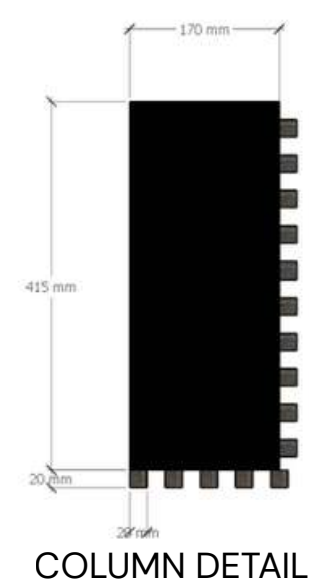






PROJECT 02

Pavillon dining space

Year 2024

Project Residential

A semi-outdoor dining area designed to blur the boundaries between indoor and outdoor. The wooden slatted roof filters sunlight beautifully throughout the day, casting soft shadows that bring the space to life. Natural materials and neutral tones create a warm *Japandi* atmosphere — perfect for gathering, cooking, and enjoying slow moments surrounded by natural light and greenery.

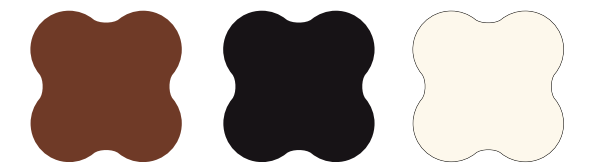
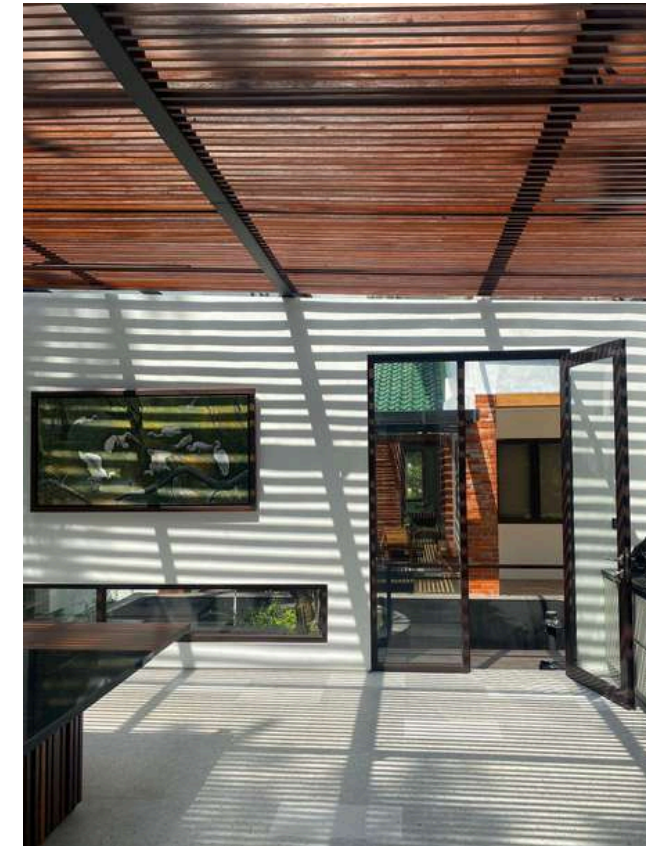
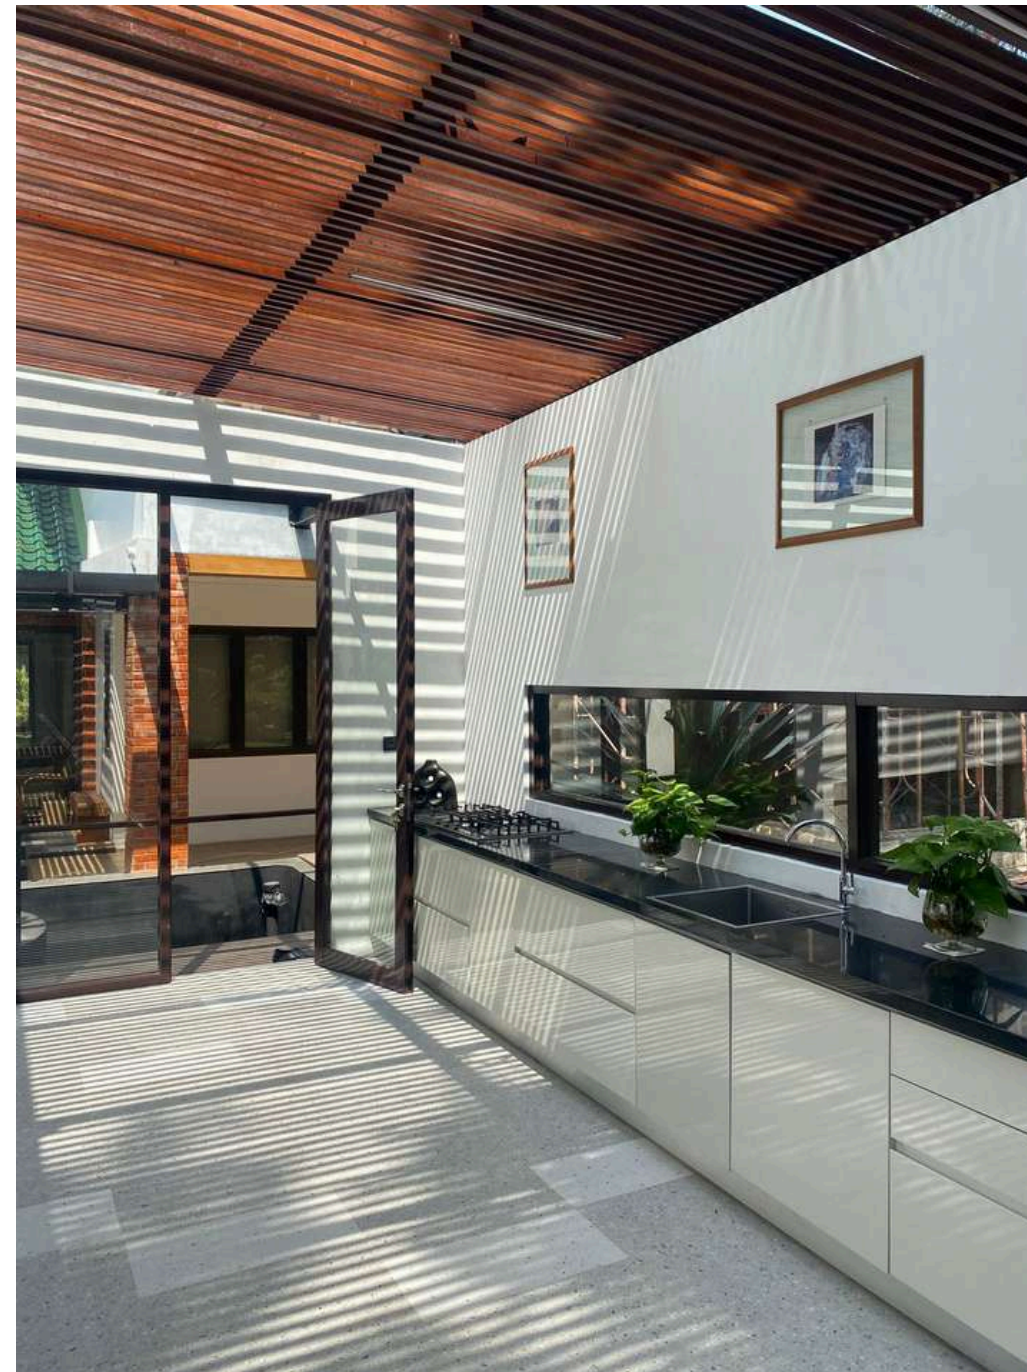


PROJECT 03







Countryside villa bedroom

Year 2024
Project Residential

A peaceful space that feels warm and embrace simplicity. Woven details, natural wood tones, and gentle light from large openings enhance the connection between interior comfort and surroundings.

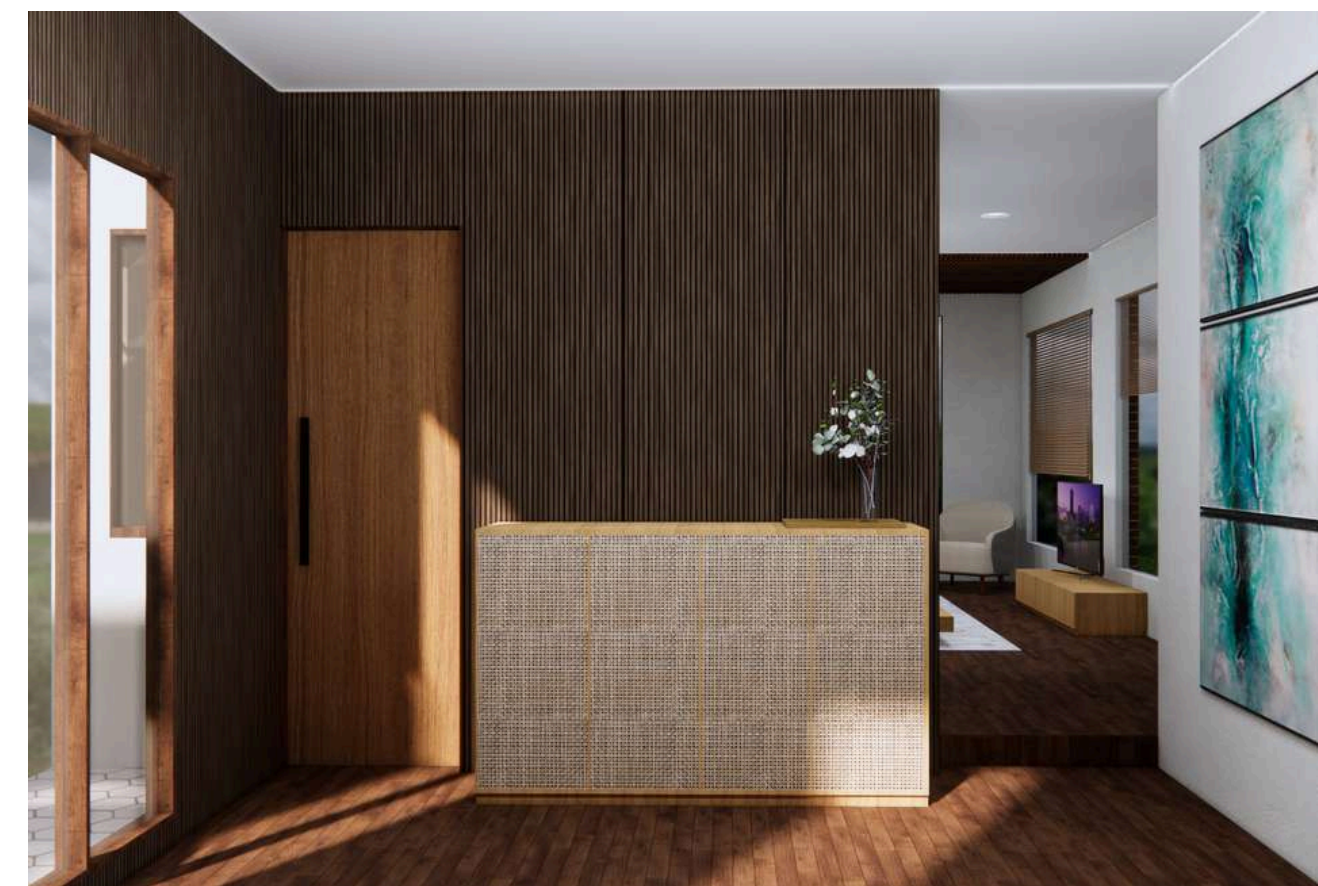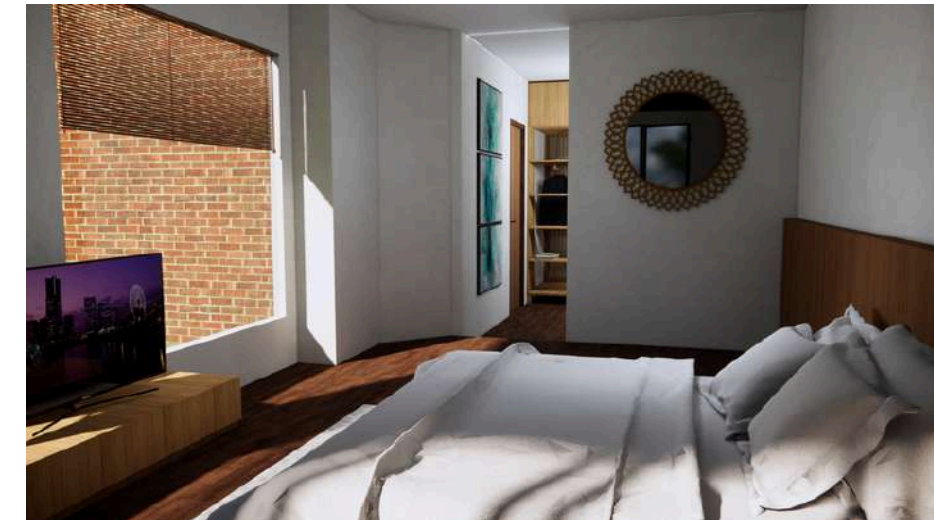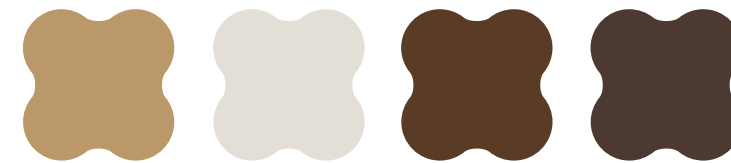

Technical drawings – Plan layout and Section

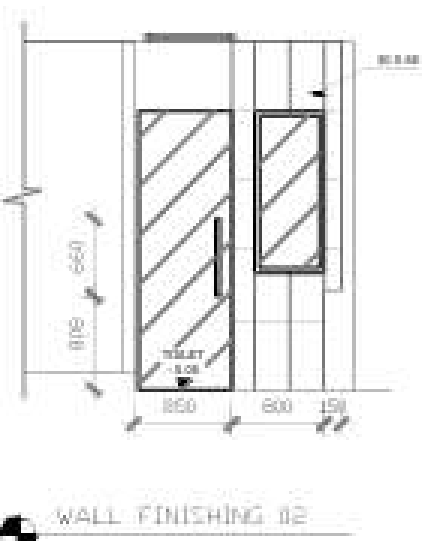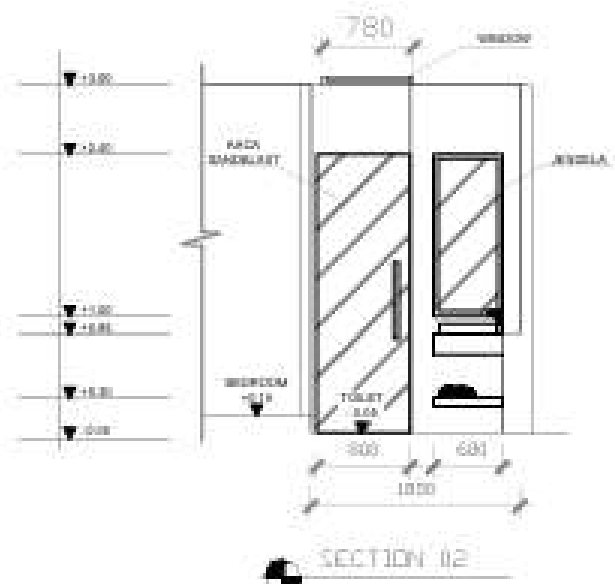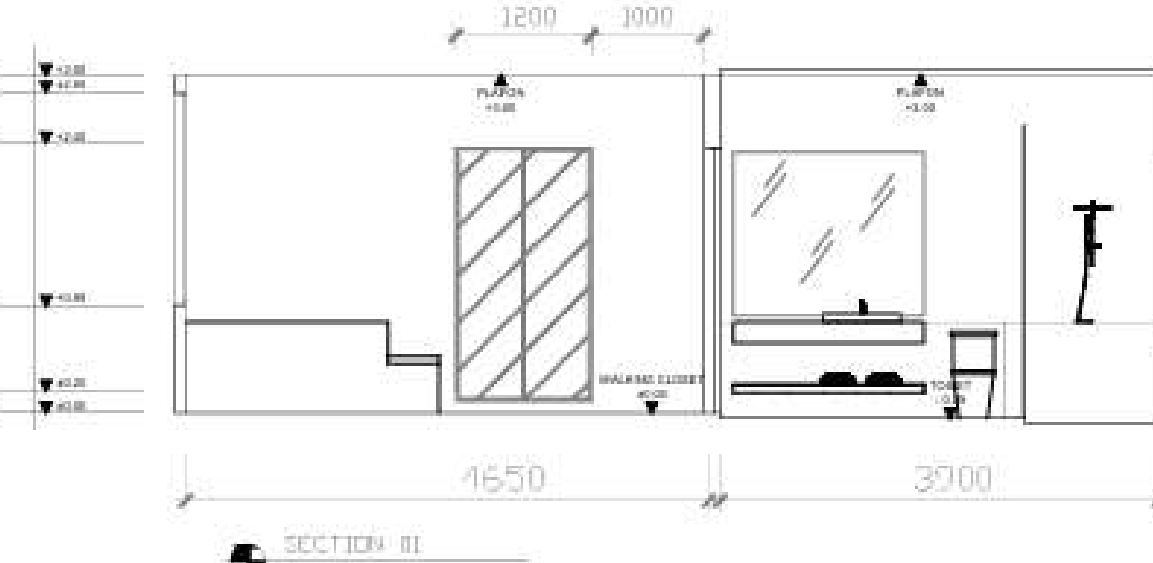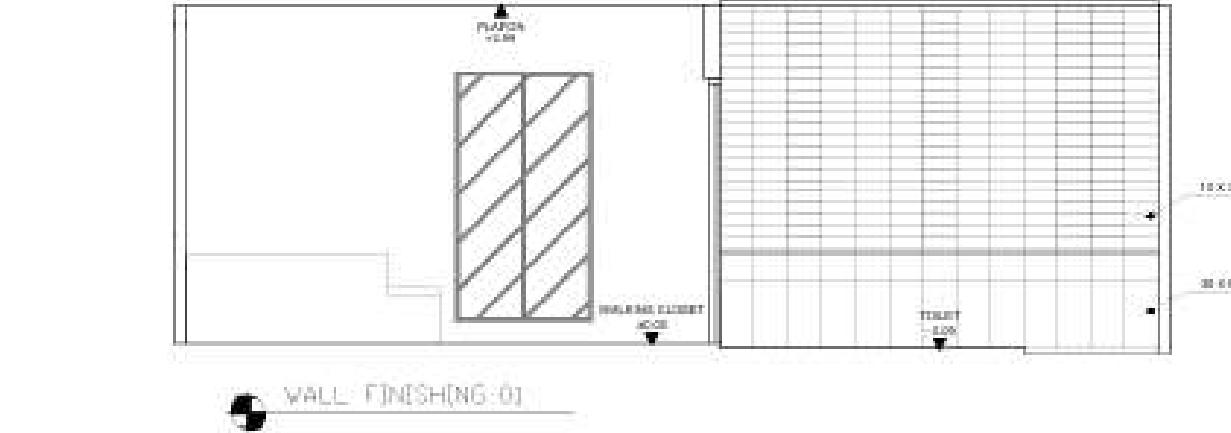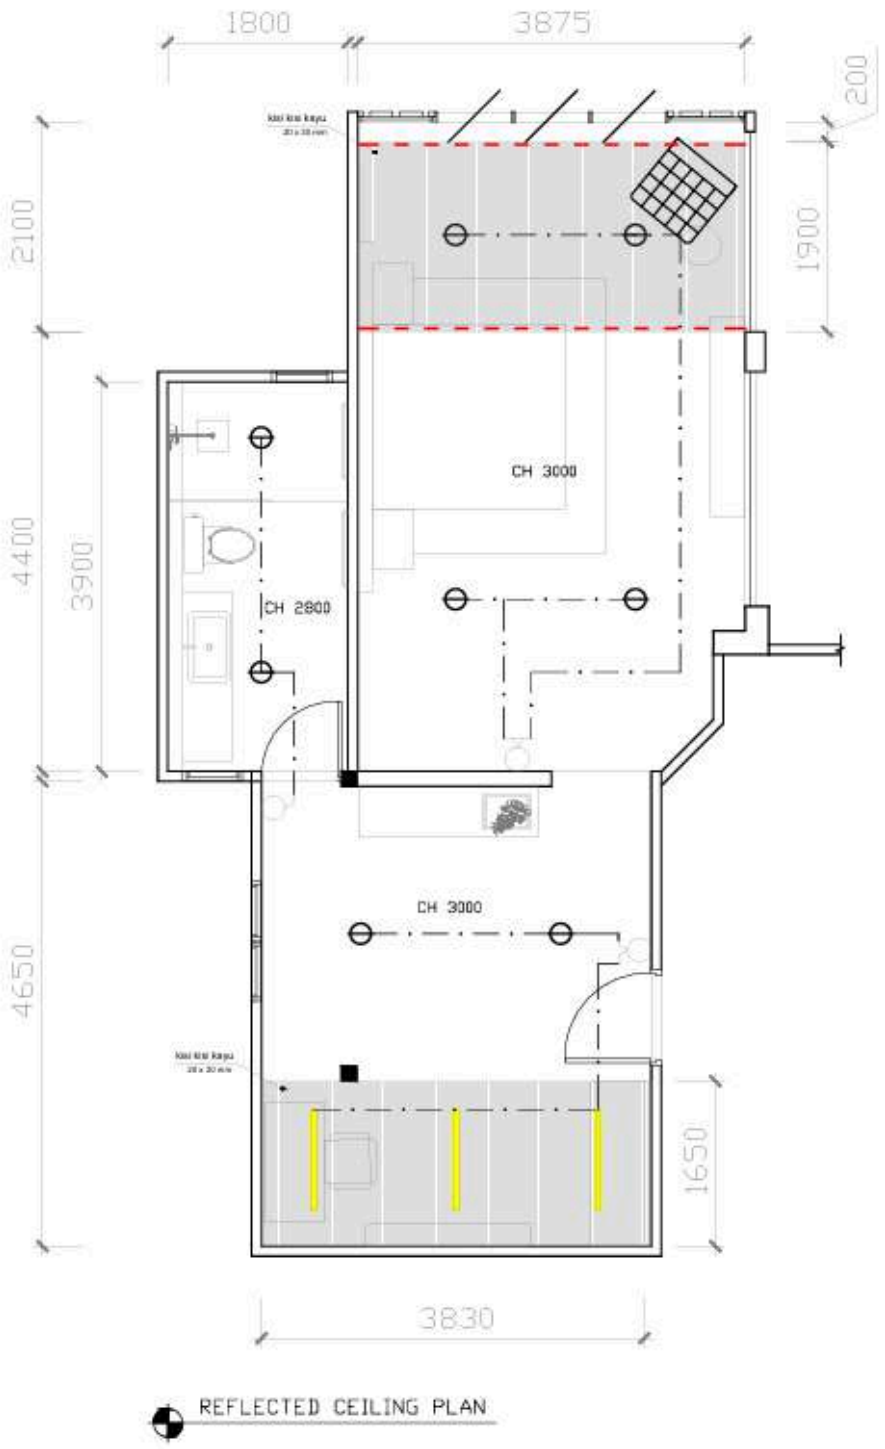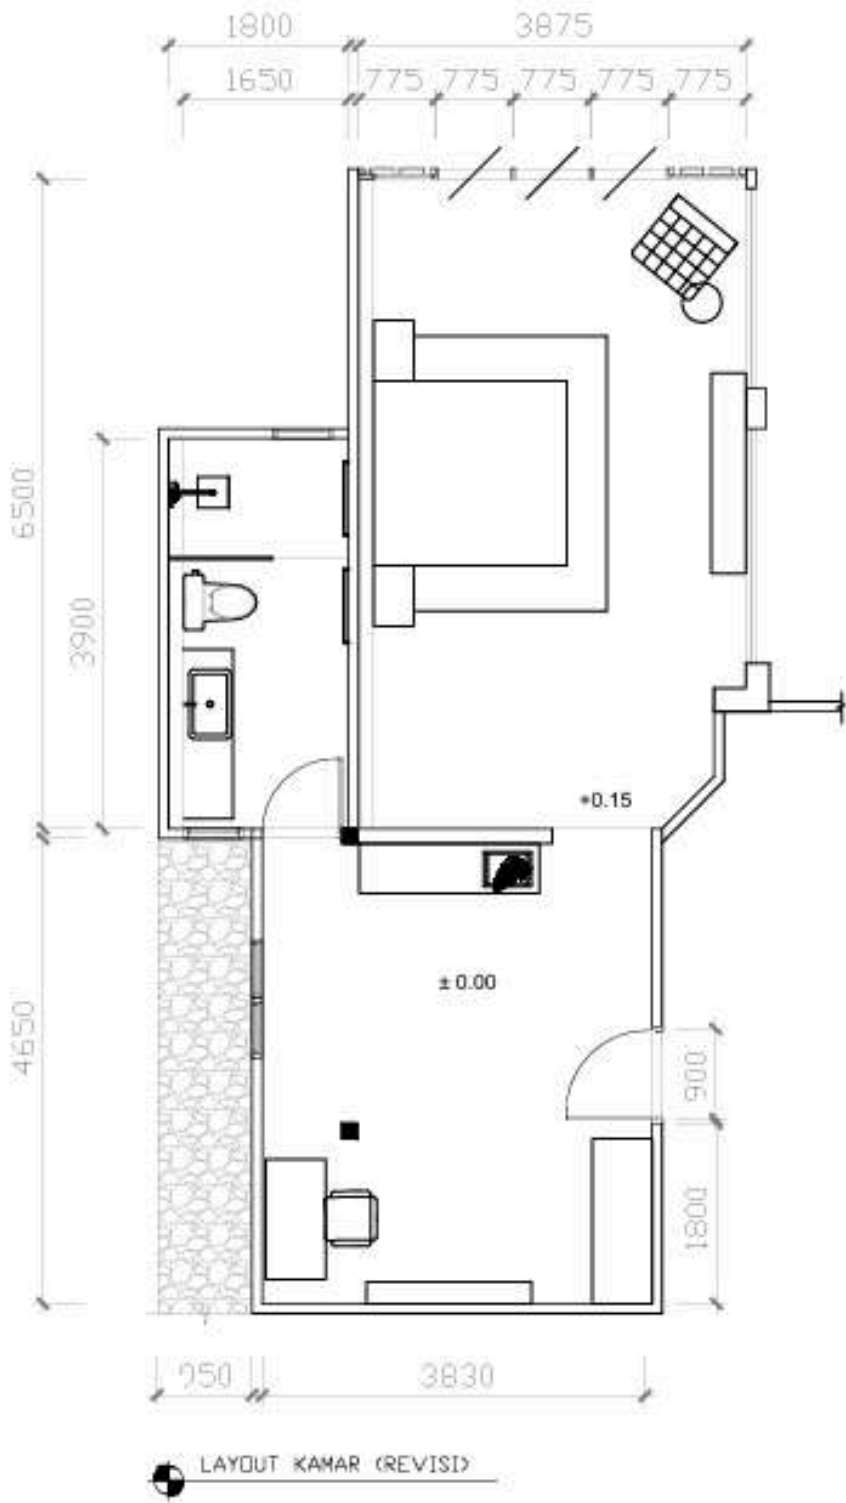



PROJECT 04



Inhouse corporate project

Year 2024



Project Office

Compilation of Arwana’s In-House Projects. A collection of innovative designs developed and managed internally to meet the company’s functional and creative needs.



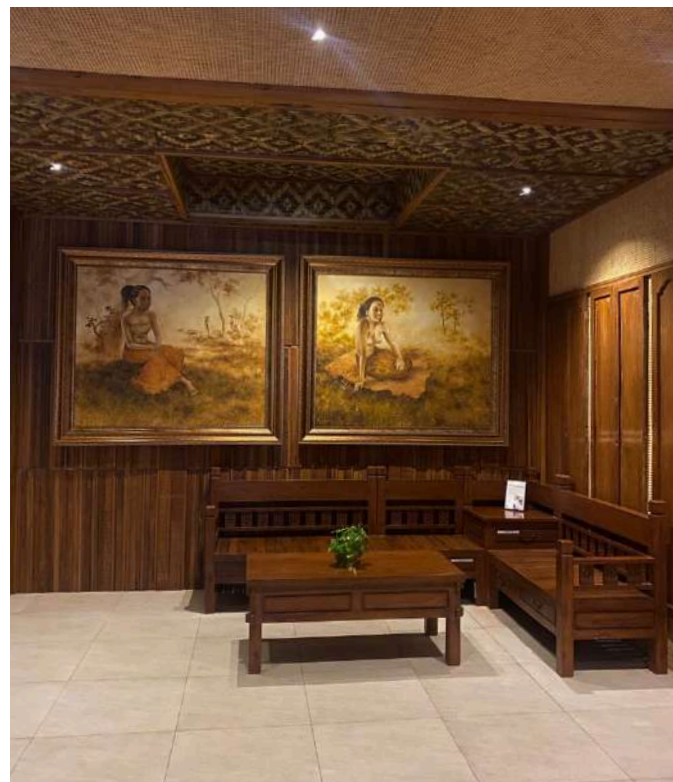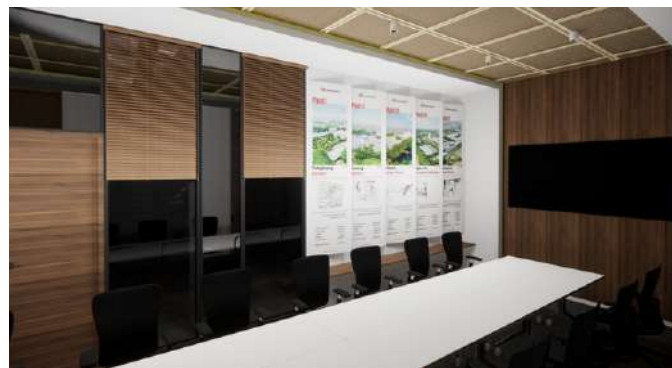

Head office renovation project highlighting local materials and inspired by Indonesia's nature and craftsmanship. The design creates a warm, calming workspace with repurposed wood pallets from our factory. I provided the 3D visualization and layout plans for this project.

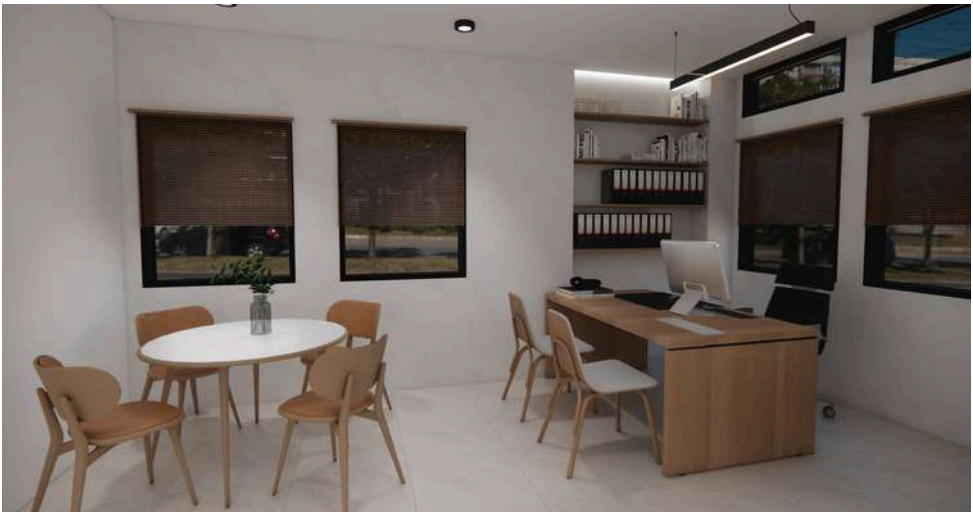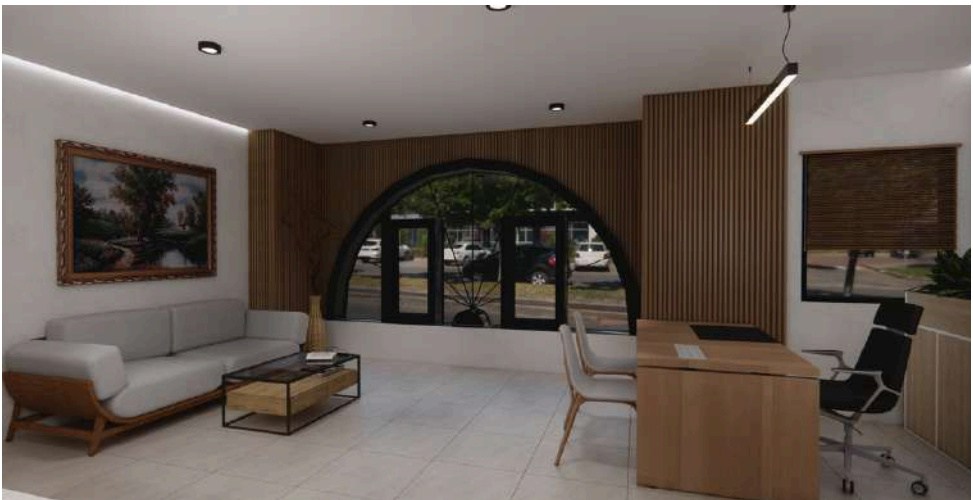

Granite pattern consultant, for external project






Showroom Tile Layout Redesign

Marketing office redesign

A renovation project for multiple staff canteens and kitchen across the factory sites, designed to create a more comfortable dining environment for staff.

Arna's catalog

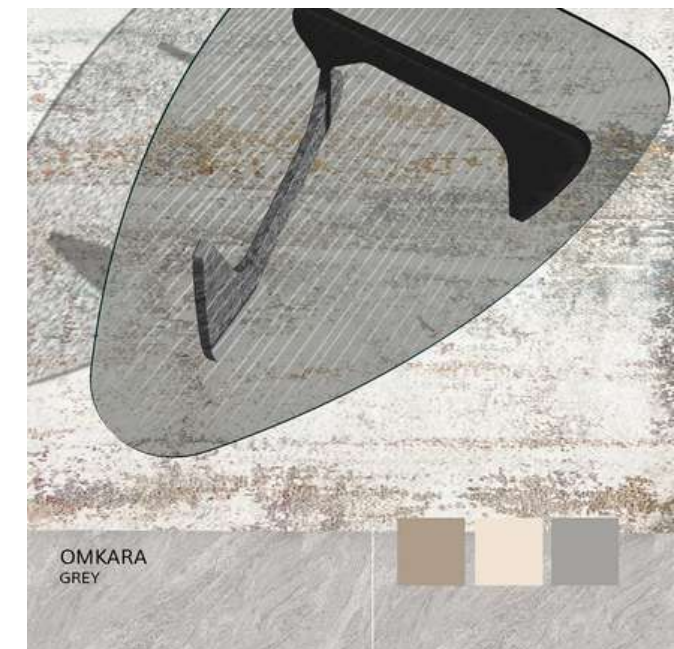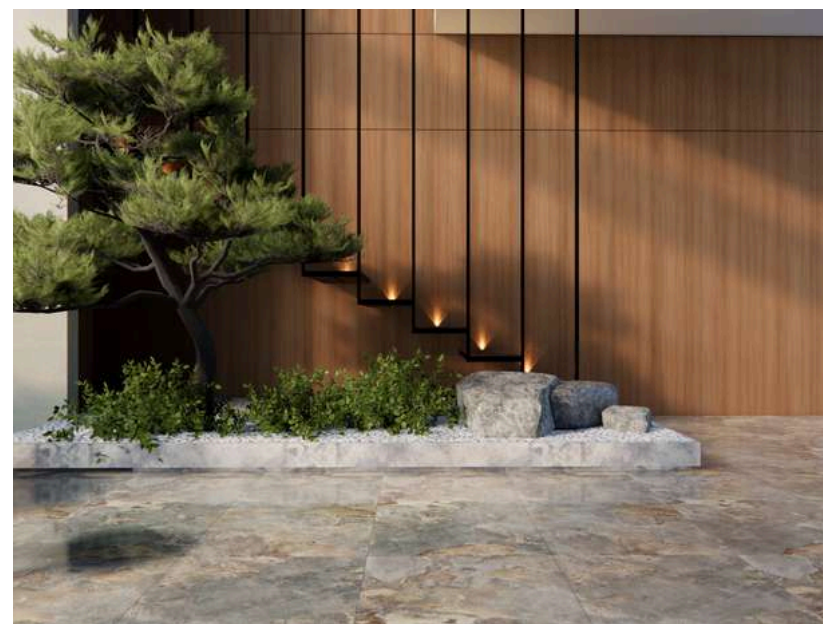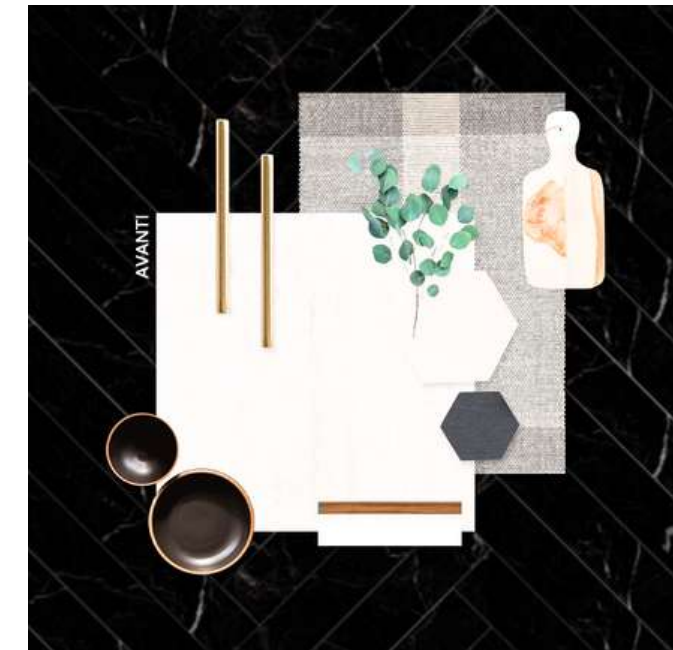

Arna's Celestine – Floor tile

Arna's Padma– Floor tile

Arna's Malaka– Floor tile

Arna granite **marketing project**, contributed design ideas and aesthetic references to the team, and created 3D renderings for catalog purposes.

PROJECT 05

Vintage photobox installation

Year 2024

Project design competition (winner)


An installation competition exploring vintage aesthetics through spatial design. The project combines nostalgic charm with interactive elements, creating a warm and memorable visual experience.



Classic style photo box, with elegant touch of velvet curtain and antique polished dark wood.



Vintage styled photo box with antique material such as aluminum and dark walnut laminated wood, with black and white scheme to bring out nostalgic vibes

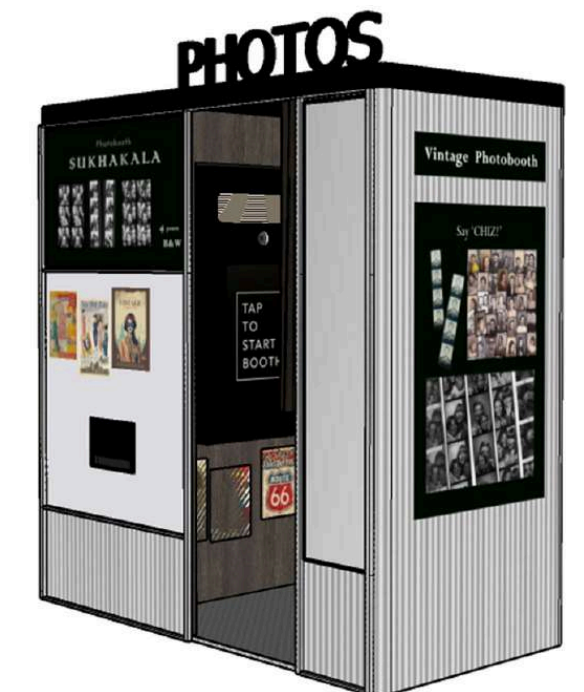

PROJECT 06

Blossom Affair

Year 2025

Project Concept project

A sweet yet elegant-vintage installation that blends pastel florals, artificial vines, and structured geometry to create a romantic yet refined atmosphere. The design highlights each bag to stand out as centerpiece within the romantic display.





PROJECT 07

Matcha Café

Year 2025

Project Concept project

Japandi inspired café, blends Japanese minimalism with Scandinavian warmth, featuring natural materials, soft curves, and muted tones. The Matcha bar serves as the main feature, complemented by warm wood finishes, curated fabric lighting, and a small zen garden that together evoke a serene balance and timeless simplicity.



Thank You!

Looking forward to
connect with you.